


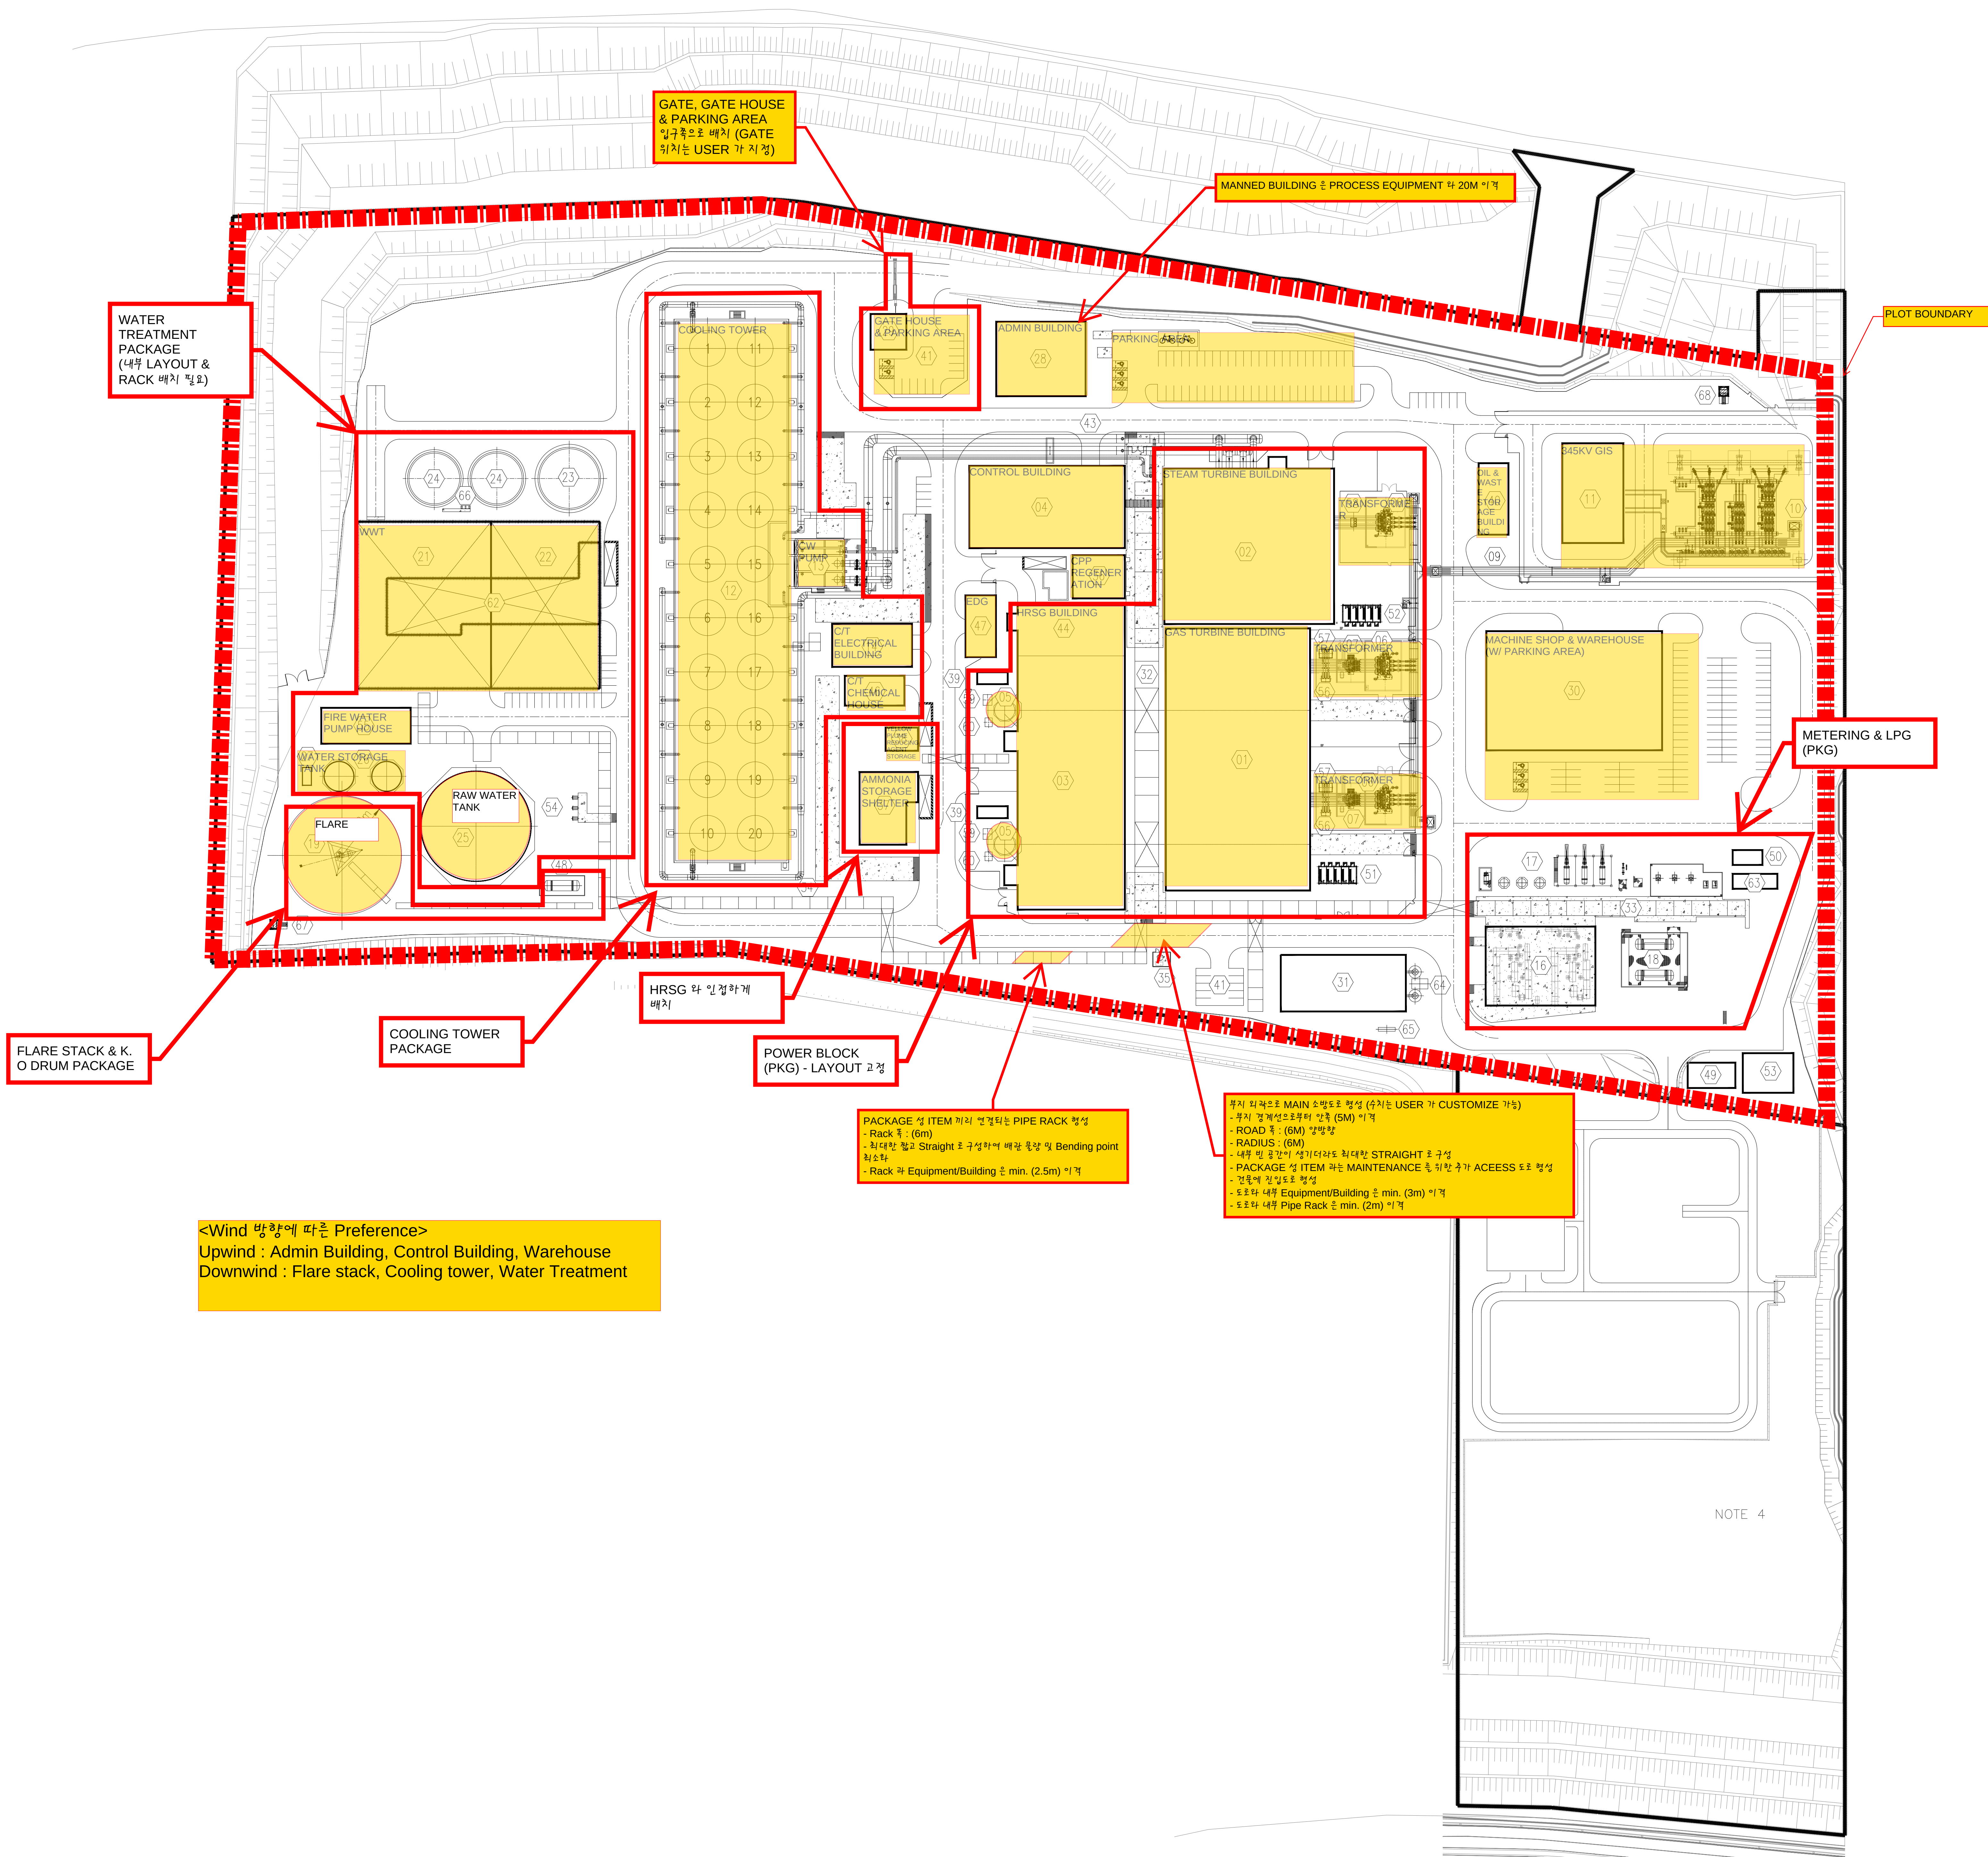

LEGEND	
NO.	DESCRIPTION
01	GAS TURBINE BUILDING
02	STEAM TURBINE BUILDING
03	HRSG BUILDING
04	CONTROL BUILDING
05	MAIN STACK
06	GAS TURBINE GENERATOR STEP-UP TRANSFORMER
07	UNIT. AUX. TRANSFORMER
08	STEAM TURBINE GENERATOR STEP-UP TRANSFORMER
09	345kV CABLE TUNNEL
10	345kV GIS
11	345kV GIS CONTROL BUILDING
12	COOLING TOWER
13	COOLING WATER PUMP STRUCTURE
14	COOLING TOWER ELECTRICAL BUILDING
15	FUEL GAS(LNG) GOVERNOR STATION(BY SK GAS)
16	FUEL GAS FINAL FILTER & PREHEATING STATION
17	LPG HEATER & VAPORIZER & BUFFER SYSTEM AREA
18	LPG SURGE DRUM
19	FLARE STACK
21	WATER & WASTE WATER TREATMENT BUILDING
22	CHEMICAL STORAGE TANK FOR WT/WWT
23	CLARIFIER FOR WWT
24	CLARIFIER FOR RW
25	RAW WATER STORAGE TANK
26	DEMI. WATER STORAGE TANK
27	POTABLE WATER STORAGE TANK
28	ADMINISTRATION BUILDING
29	GATE HOUSE
30	MACHINE SHOP & WAREHOUSE
31	AUX. & LPG HOT WATER BOILER BUILDING
32	MAIN PIPE RACK
33	FUEL GAS PIPE RACK
34	UTILITY PIPE RACK
35	N2 GAS STORAGE TANK AREA
36	CPP REGENERATION PLANT
37	AQUEOUS AMMONIA STORAGE SHELTER
38	YELLOW PLUME REDUCING AGENT STORAGE
39	SCR VAPORIZER AND FAN
40	OIL & WASTE STORAGE BUILDING
41	PARKING AREA
43	COOLING WATER CONDUIT
44	BOILER FEED WATER PUMP AREA
45	TRANSMISSION TOWER
46	COOLING TOWER CHEMICAL INJECTION HOUSE
47	EDG BUILDING
48	FLARE K.O DRUM
49	RAW WATER BUFFER POND
50	N2 GAS GENERATOR FOR FLARE SYSTEM
51	FIRE FIGHTING GAS SUPPLY BUILDING FOR GAS TURBINE BUILDING #1
52	FIRE FIGHTING GAS SUPPLY BUILDING FOR GAS TURBINE BUILDING #2
53	LNG FILTER/SEPARATER
54	RAW WATER SUPPLY PUMP
55	FIRE WATER PUMP HOUSE
56	SEE TRANSFORMER FOR GT
57	SFC TRANSFORMER FOR GT
58	SEE TRANSFORMER FOR ST
59	CEMS
60	CO/THC ANALYZER SYSTEM
62	WT/WWT PUMP ROOM
63	LPG METERING SKID
64	TMS SHELTER
65	GAS PRESSURE REGULATING SYSTEM
66	SLUDGE TRANSFER PUMPS
67	WATCH TOWER #1
68	WATCH TOWER #2